

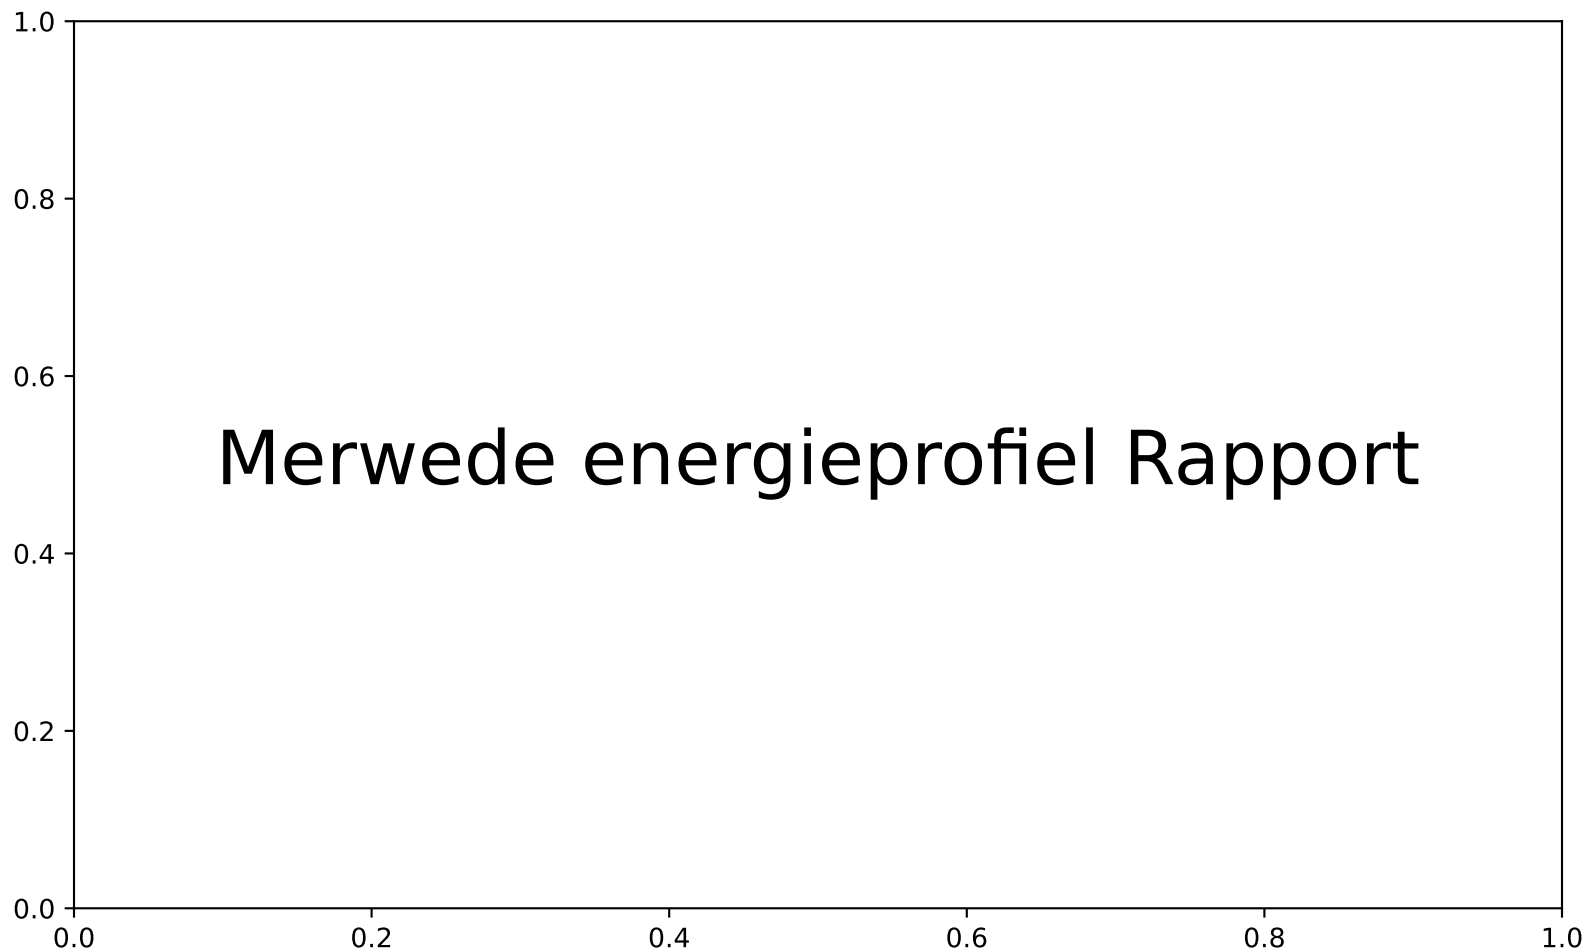


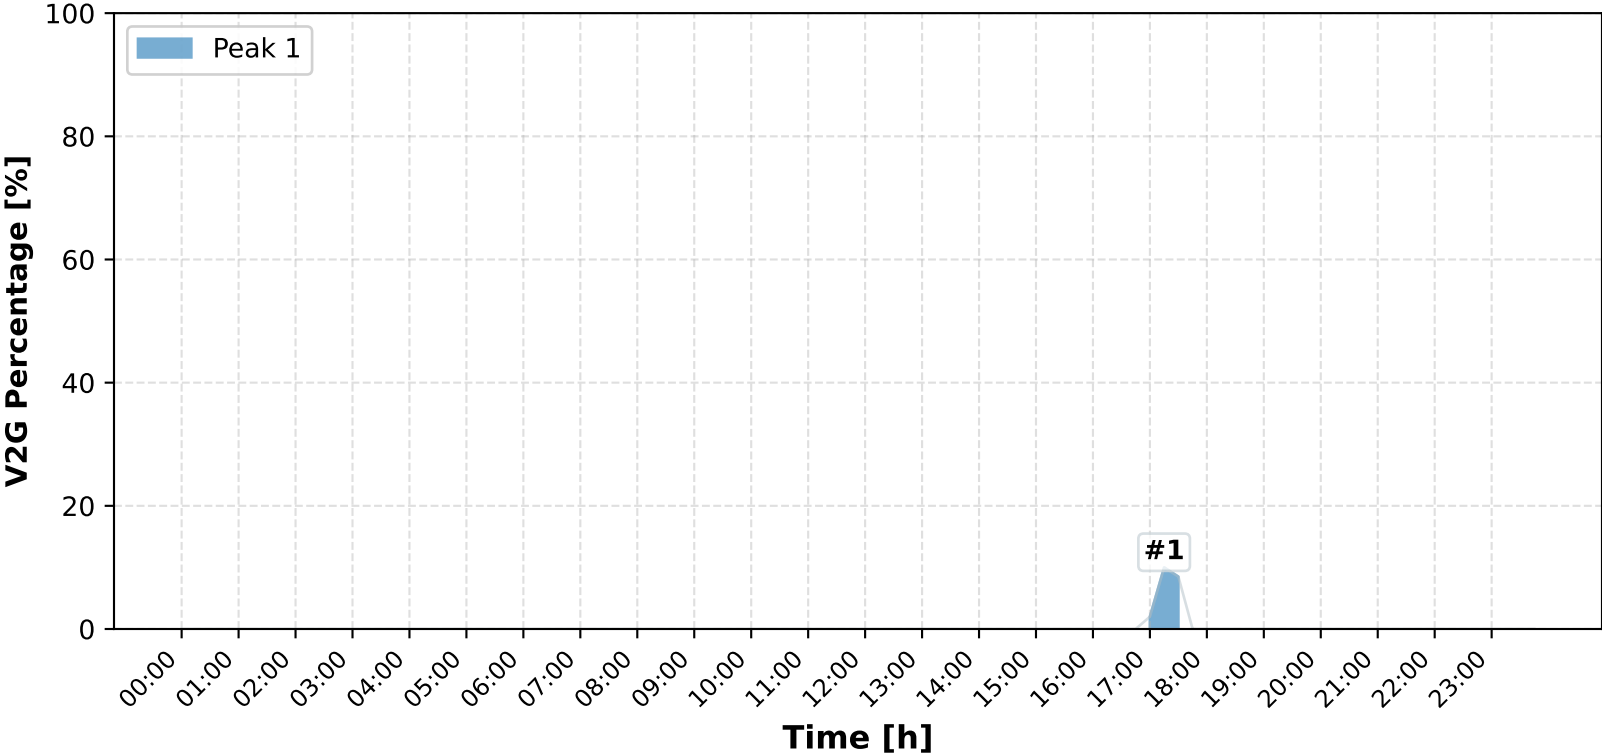

profile_average - Profile & Excess

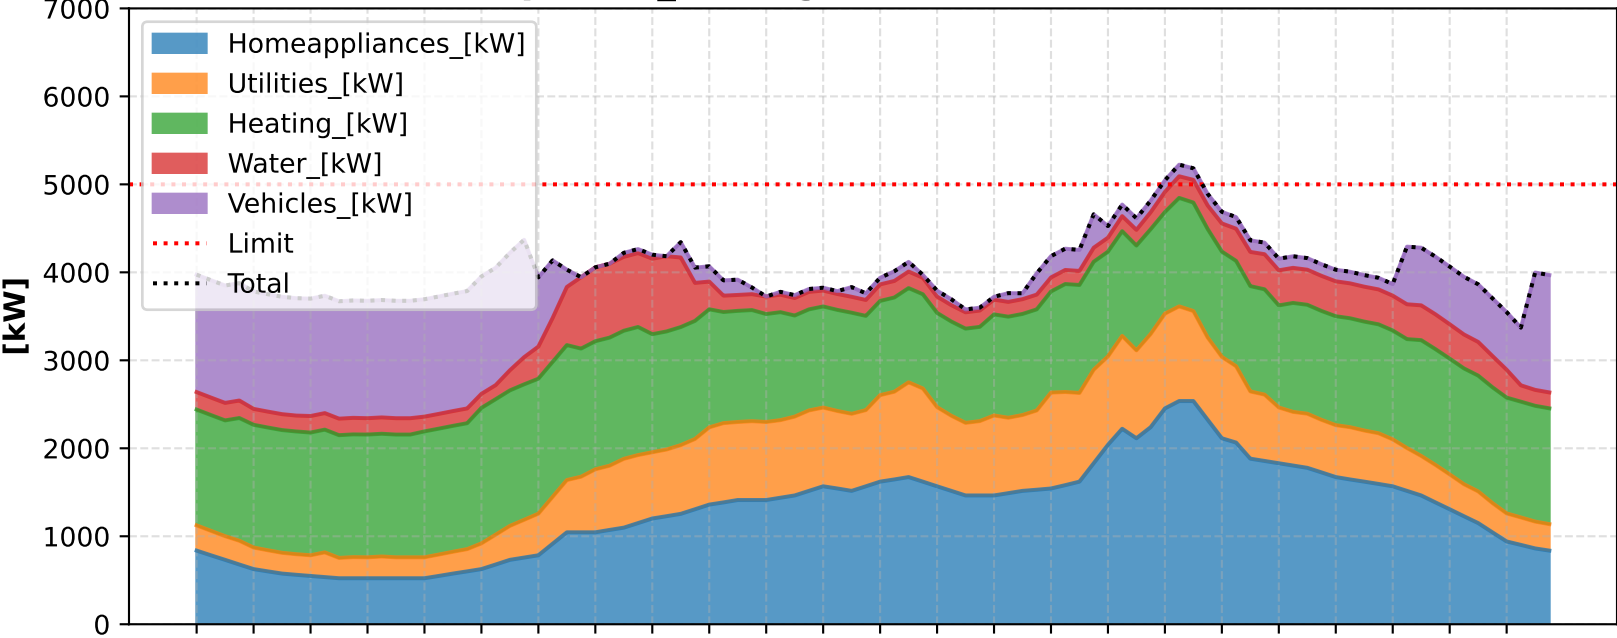

Peak	Start	End	Cars Needed	Energy [kWh]	Min Avg Battery [%]
1	17:00:00	17:30:00	20	113.05	14.13

Dimensie: No V2G, No N-1

Categorie	Spanning & Grens	Parameters	Afmetingen (B x L x H)	Aantal
MS Transformator	Primair: 110 kV\Secundair: 10.0 kV Grens: 2500 kVA	Schakeling: YNd11 Korstluitspanning: 11% Kortsluitverlies: 19000 W	B: 1800 mm L: 2200 mm H: 2400 mm	3
LS Transformator	Primair: 10 kV\Secundair: 0.4 kV Grens: 630 kVA	Schakeling: Dyn11 Korstluitspanning: 4% Kortsluitverlies: 6500 W	B: 950 mm L: 1600 mm H: 1800 mm	12

Categorie	Spanning & Materiaal	Doorsnede & Aders	Parameters & Spanningsval	Kabels per Trafo
MS Cable	Spanning: 10.0 kV Materiaal: Aluminium	Doorsnede: 50 mm² Ader Aantal: 3	Max Amperage: 145 A Weerstand: 0.641 Ω/km Spanningsval: 186.0 V	1 per Trafo
LS Cable	Spanning: 0.4 kV Materiaal: Aluminium	Doorsnede: 240 mm² Ader Aantal: 4	Max Amperage: 300 A Weerstand: 0.125 Ω/km Spanningsval: 387.5 V	3 per Trafo

Dimensie: No V2G, N-1

Categorie	Spanning & Grens	Parameters	Afmetingen (B x L x H)	Aantal
MS Transformator	Primair: 110 kV\Secundair: 10.0 kV Grens: 4000 kVA	Schakeling: YNd11 Korstluitspanning: 11% Kortsluitverlies: 28000 W	B: 2000 mm L: 2500 mm H: 2600 mm	3
LS Transformator	Primair: 10 kV\Secundair: 0.4 kV Grens: 1000 kVA	Schakeling: Dyn11 Korstluitspanning: 6% Kortsluitverlies: 9000 W	B: 1050 mm L: 1800 mm H: 2100 mm	12

Categorie	Spanning & Materiaal	Doorsnede & Aders	Parameters & Spanningsval	Kabels per Trafo
MS Cable	Spanning: 10.0 kV Materiaal: Aluminium	Doorsnede: 95 mm² Ader Aantal: 3	Max Amperage: 210 A Weerstand: 0.32 Ω/km Spanningsval: 139.3 V	2 per Trafo
LS Cable	Spanning: 0.4 kV Materiaal: Koper	Doorsnede: 185 mm² Ader Aantal: 4	Max Amperage: 360 A Weerstand: 0.0991 Ω/km Spanningsval: 258.0 V	6 per Trafo

Dimensie: V2G, No N-1

Categorie	Spanning & Grens	Parameters	Afmetingen (B x L x H)	Aantal
MS Transformator	Primair: 110 kV\Secundair: 10.0 kV Grens: 2500 kVA	Schakeling: YNd11 Korstluitspanning: 11% Kortsluitverlies: 19000 W	B: 1800 mm L: 2200 mm H: 2400 mm	3
LS Transformator	Primair: 10 kV\Secundair: 0.4 kV Grens: 630 kVA	Schakeling: Dyn11 Korstluitspanning: 4% Kortsluitverlies: 6500 W	B: 950 mm L: 1600 mm H: 1800 mm	12



Categorie	Spanning & Materiaal	Doorsnede & Aders	Parameters & Spanningsval	Kabels per Trafo
MS Cable	Spanning: 10.0 kV Materiaal: Aluminium	Doorsnede: 50 mm² Ader Aantal: 3	Max Amperage: 145 A Weerstand: 0.641 Ω/km Spanningsval: 178.1 V	1 per Trafo
LS Cable	Spanning: 0.4 kV Materiaal: Aluminium	Doorsnede: 185 mm² Ader Aantal: 4	Max Amperage: 230 A Weerstand: 0.164 Ω/km Spanningsval: 370.9 V	3 per Trafo

Dimensie: V2G, N-1

Categorie	Spanning & Grens	Parameters	Afmetingen (B x L x H)	Aantal
MS Transformator	Primair: 110 kV\Secundair: 10.0 kV Grens: 4000 kVA	Schakeling: YNd11 Korstluitspanning: 11% Kortsluitverlies: 28000 W	B: 2000 mm L: 2500 mm H: 2600 mm	3
LS Transformator	Primair: 10 kV\Secundair: 0.4 kV Grens: 630 kVA	Schakeling: Dyn11 Korstluitspanning: 4% Kortsluitverlies: 6500 W	B: 950 mm L: 1600 mm H: 1800 mm	12

Categorie	Spanning & Materiaal	Doorsnede & Aders	Parameters & Spanningsval	Kabels per Trafo
MS Cable	Spanning: 10.0 kV Materiaal: Aluminium	Doorsnede: 95 mm² Ader Aantal: 3	Max Amperage: 210 A Weerstand: 0.32 Ω/km Spanningsval: 133.3 V	2 per Trafo
LS Cable	Spanning: 0.4 kV Materiaal: Aluminium	Doorsnede: 240 mm² Ader Aantal: 4	Max Amperage: 300 A Weerstand: 0.125 Ω/km Spanningsval: 246.9 V	6 per Trafo

profile_best - Profile & Excess

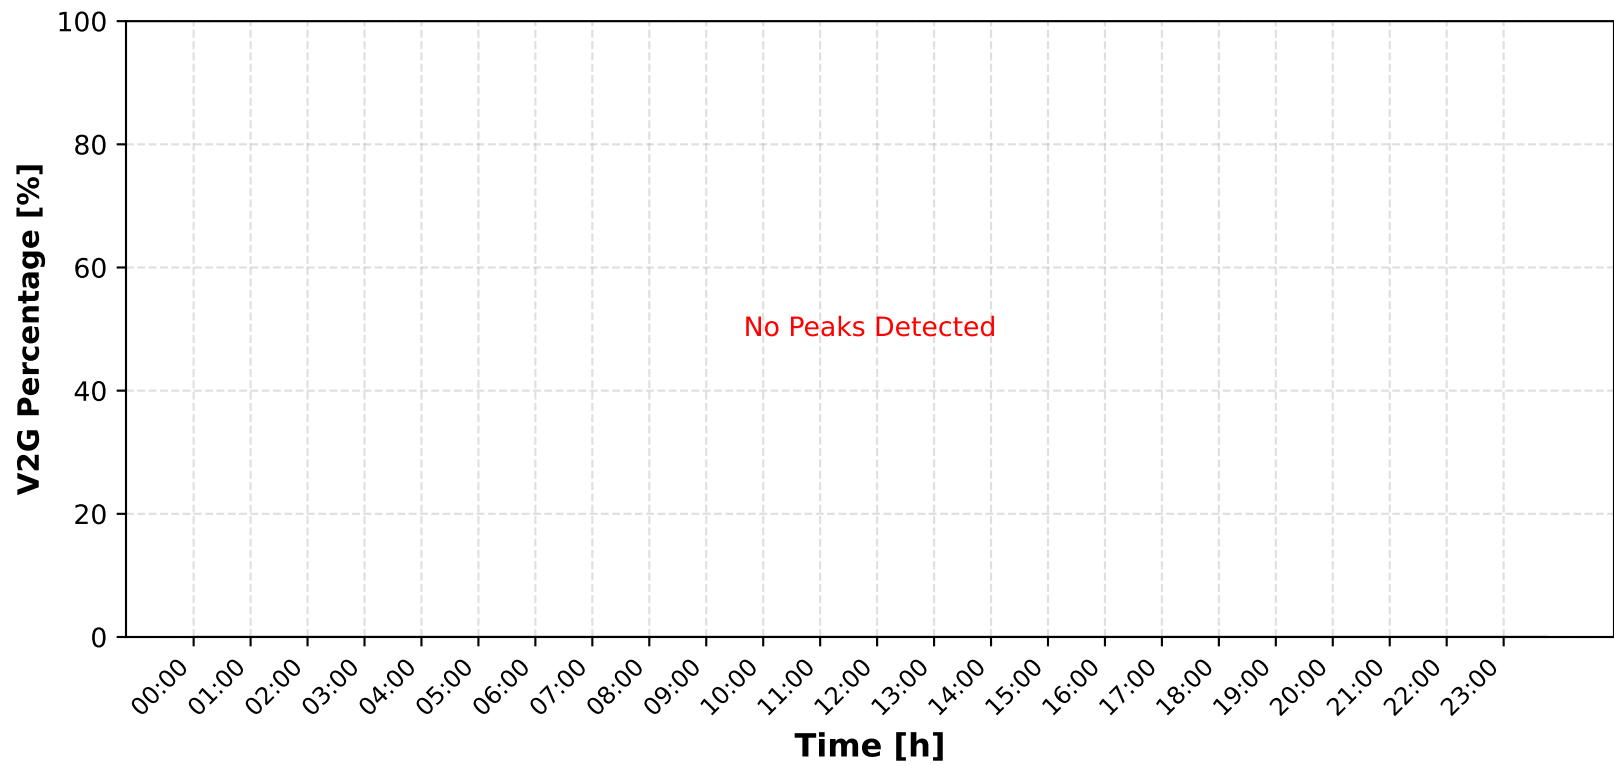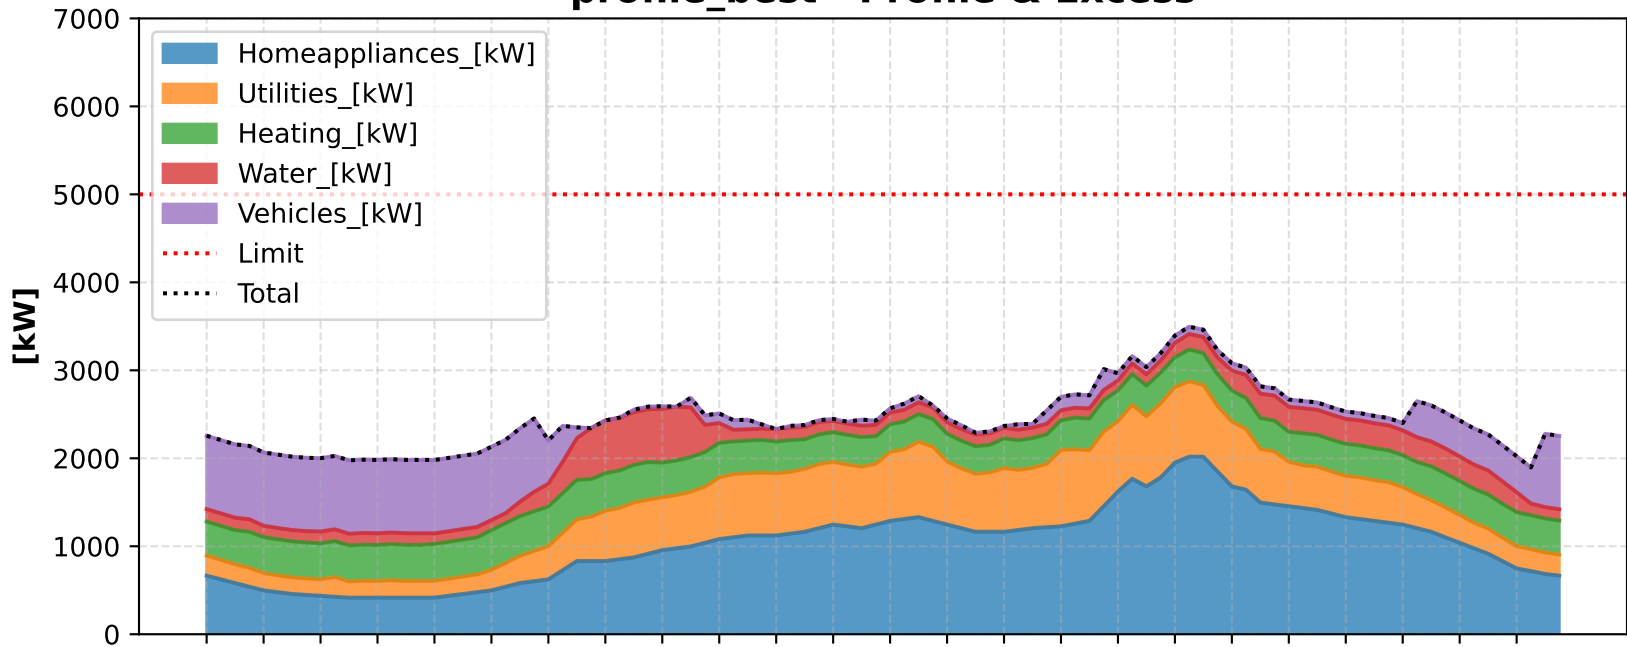

Dimensie: No V2G, No N-1

Categorie	Spanning & Grens	Parameters	Afmetingen (B x L x H)	Aantal
MS Transformator	Primair: 110 kV\\Secundair: 10.0 kV Grens: 2500 kVA	Schakeling: YNd11 Korstluitspanning: 11% Kortsluitverlies: 19000 W	B: 1800 mm L: 2200 mm H: 2400 mm	3
LS Transformator	Primair: 10 kV\\Secundair: 0.4 kV Grens: 400 kVA	Schakeling: Dyn11 Korstluitspanning: 4% Kortsluitverlies: 4500 W	B: 850 mm L: 1450 mm H: 1600 mm	12

Categorie	Spanning & Materiaal	Doorsnede & Aders	Parameters & Spanningsval	Kabels per Trafo
MS Cable	Spanning: 10.0 kV Materiaal: Aluminium	Doorsnede: 50 mm² Ader Aantal: 3	Max Amperage: 145 A Weerstand: 0.641 Ω/km Spanningsval: 124.5 V	1 per Trafo
LS Cable	Spanning: 0.4 kV Materiaal: Aluminium	Doorsnede: 150 mm² Ader Aantal: 4	Max Amperage: 188 A Weerstand: 0.206 Ω/km Spanningsval: 259.3 V	3 per Trafo

Dimensie: No V2G, N-1

Categorie	Spanning & Grens	Parameters	Afmetingen (B x L x H)	Aantal
MS Transformator	Primair: 110 kV\\Secundair: 10.0 kV Grens: 2500 kVA	Schakeling: YNd11 Korstluitspanning: 11% Kortsluitverlies: 19000 W	B: 1800 mm L: 2200 mm H: 2400 mm	3
LS Transformator	Primair: 10 kV\\Secundair: 0.4 kV Grens: 630 kVA	Schakeling: Dyn11 Korstluitspanning: 4% Kortsluitverlies: 6500 W	B: 950 mm L: 1600 mm H: 1800 mm	12

Categorie	Spanning & Materiaal	Doorsnede & Aders	Parameters & Spanningsval	Kabels per Trafo
MS Cable	Spanning: 10.0 kV Materiaal: Aluminium	Doorsnede: 50 mm² Ader Aantal: 3	Max Amperage: 145 A Weerstand: 0.641 Ω/km Spanningsval: 186.7 V	2 per Trafo
LS Cable	Spanning: 0.4 kV Materiaal: Aluminium	Doorsnede: 185 mm² Ader Aantal: 4	Max Amperage: 230 A Weerstand: 0.164 Ω/km Spanningsval: 345.8 V	6 per Trafo

Dimensie: V2G, No N-1

Categorie	Spanning & Grens	Parameters	Afmetingen (B x L x H)	Aantal
MS Transformator	Primair: 110 kV\\Secundair: 10.0 kV Grens: 2500 kVA	Schakeling: YNd11 Korstluitspanning: 11% Kortsluitverlies: 19000 W	B: 1800 mm L: 2200 mm H: 2400 mm	3
LS Transformator	Primair: 10 kV\\Secundair: 0.4 kV Grens: 400 kVA	Schakeling: Dyn11 Korstluitspanning: 4% Kortsluitverlies: 4500 W	B: 850 mm L: 1450 mm H: 1600 mm	12



Categorie	Spanning & Materiaal	Doorsnede & Aders	Parameters & Spanningsval	Kabels per Trafo
MS Cable	Spanning: 10.0 kV Materiaal: Aluminium	Doorsnede: 50 mm² Ader Aantal: 3	Max Amperage: 145 A Weerstand: 0.641 Ω/km Spanningsval: 124.5 V	1 per Trafo
LS Cable	Spanning: 0.4 kV Materiaal: Aluminium	Doorsnede: 150 mm² Ader Aantal: 4	Max Amperage: 188 A Weerstand: 0.206 Ω/km Spanningsval: 259.3 V	3 per Trafo

Dimensie: V2G, N-1

Categorie	Spanning & Grens	Parameters	Afmetingen (B x L x H)	Aantal
MS Transformator	Primair: 110 kV\\Secundair: 10.0 kV Grens: 2500 kVA	Schakeling: YNd11 Korstluitspanning: 11% Kortsluitverlies: 19000 W	B: 1800 mm L: 2200 mm H: 2400 mm	3
LS Transformator	Primair: 10 kV\\Secundair: 0.4 kV Grens: 630 kVA	Schakeling: Dyn11 Korstluitspanning: 4% Kortsluitverlies: 6500 W	B: 950 mm L: 1600 mm H: 1800 mm	12

Categorie	Spanning & Materiaal	Doorsnede & Aders	Parameters & Spanningsval	Kabels per Trafo
MS Cable	Spanning: 10.0 kV Materiaal: Aluminium	Doorsnede: 50 mm² Ader Aantal: 3	Max Amperage: 145 A Weerstand: 0.641 Ω/km Spanningsval: 186.7 V	2 per Trafo
LS Cable	Spanning: 0.4 kV Materiaal: Aluminium	Doorsnede: 185 mm² Ader Aantal: 4	Max Amperage: 230 A Weerstand: 0.164 Ω/km Spanningsval: 345.8 V	6 per Trafo

profile_worst - Profile & Excess

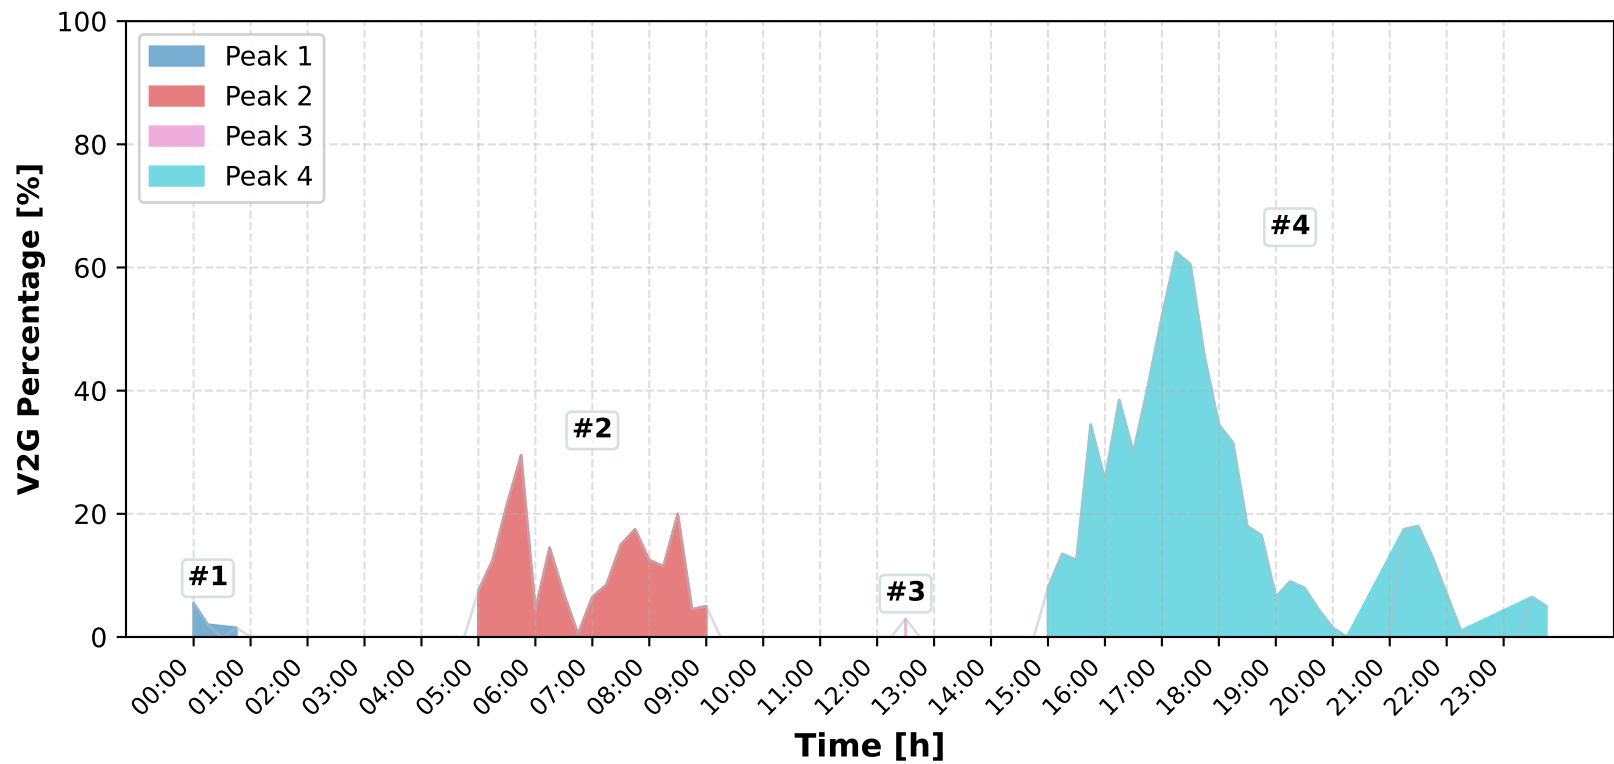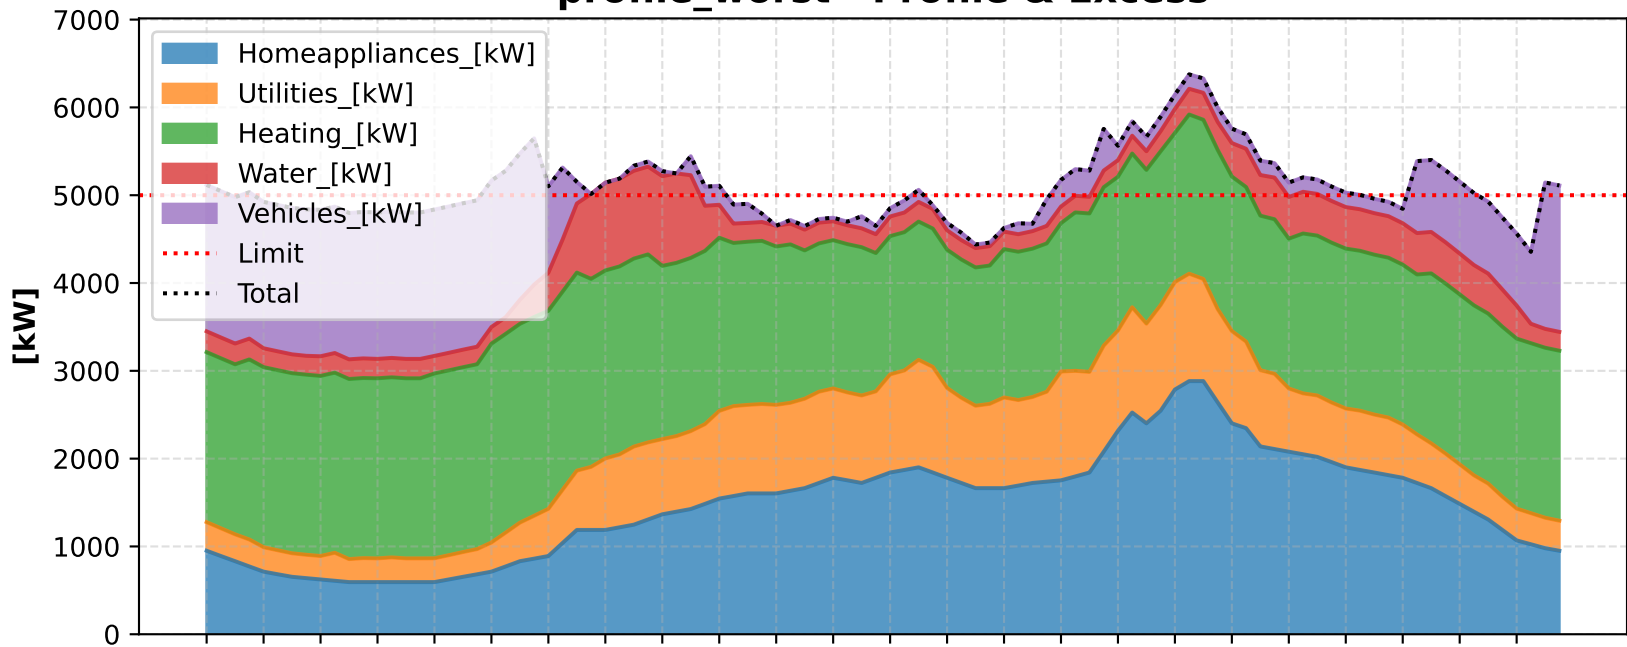

Peak	Start	End	Cars Needed	Energy [kWh]	Min Avg Battery [%]
1	00:00:00	00:45:00	11	49.55	11.26
2	05:00:00	09:00:00	59	1092.98	46.31
3	12:30:00	12:30:00	6	15.43	6.43
4	15:00:00	23:45:00	125	3425.17	68.5

Dimensie: No V2G, No N-1

Categorie	Spanning & Grens	Parameters	Afmetingen (B x L x H)	Aantal
MS Transformator	Primair: 110 kV\\Secundair: 10.0 kV Grens: 2500 kVA	Schakeling: YNd11 Korstluitspanning: 11% Kortsluitverlies: 19000 W	B: 1800 mm L: 2200 mm H: 2400 mm	3
LS Transformator	Primair: 10 kV\\Secundair: 0.4 kV Grens: 630 kVA	Schakeling: Dyn11 Korstluitspanning: 4% Kortsluitverlies: 6500 W	B: 950 mm L: 1600 mm H: 1800 mm	12

Categorie	Spanning & Materiaal	Doorsnede & Aders	Parameters & Spanningsval	Kabels per Trafo
MS Cable	Spanning: 10.0 kV Materiaal: Aluminium	Doorsnede: 50 mm² Ader Aantal: 3	Max Amperage: 145 A Weerstand: 0.641 Ω/km Spanningsval: 227.1 V	1 per Trafo
LS Cable	Spanning: 0.4 kV Materiaal: Aluminium	Doorsnede: 240 mm² Ader Aantal: 4	Max Amperage: 300 A Weerstand: 0.125 Ω/km Spanningsval: 473.0 V	3 per Trafo

Dimensie: No V2G, N-1

Categorie	Spanning & Grens	Parameters	Afmetingen (B x L x H)	Aantal
MS Transformator	Primair: 110 kV\\Secundair: 10.0 kV Grens: 4000 kVA	Schakeling: YNd11 Korstluitspanning: 11% Kortsluitverlies: 28000 W	B: 2000 mm L: 2500 mm H: 2600 mm	3
LS Transformator	Primair: 10 kV\\Secundair: 0.4 kV Grens: 1000 kVA	Schakeling: Dyn11 Korstluitspanning: 6% Kortsluitverlies: 9000 W	B: 1050 mm L: 1800 mm H: 2100 mm	12

Categorie	Spanning & Materiaal	Doorsnede & Aders	Parameters & Spanningsval	Kabels per Trafo
MS Cable	Spanning: 10.0 kV Materiaal: Aluminium	Doorsnede: 95 mm² Ader Aantal: 3	Max Amperage: 210 A Weerstand: 0.32 Ω/km Spanningsval: 170.0 V	2 per Trafo
LS Cable	Spanning: 0.4 kV Materiaal: Koper	Doorsnede: 240 mm² Ader Aantal: 4	Max Amperage: 425 A Weerstand: 0.0754 Ω/km Spanningsval: 314.9 V	6 per Trafo

Dimensie: V2G, No N-1

Categorie	Spanning & Grens	Parameters	Afmetingen (B x L x H)	Aantal
MS Transformator	Primair: 110 kV\\Secundair: 10.0 kV Grens: 2500 kVA	Schakeling: YNd11 Korstluitspanning: 11% Kortsluitverlies: 19000 W	B: 1800 mm L: 2200 mm H: 2400 mm	3
LS Transformator	Primair: 10 kV\\Secundair: 0.4 kV Grens: 630 kVA	Schakeling: Dyn11 Korstluitspanning: 4% Kortsluitverlies: 6500 W	B: 950 mm L: 1600 mm H: 1800 mm	12

Categorie	Spanning & Materiaal	Doorsnede & Aders	Parameters & Spanningsval	Kabels per Trafo
MS Cable	Spanning: 10.0 kV Materiaal: Aluminium	Doorsnede: 50 mm² Ader Aantal: 3	Max Amperage: 145 A Weerstand: 0.641 Ω/km Spanningsval: 178.1 V	1 per Trafo
LS Cable	Spanning: 0.4 kV Materiaal: Aluminium	Doorsnede: 185 mm² Ader Aantal: 4	Max Amperage: 230 A Weerstand: 0.164 Ω/km Spanningsval: 370.9 V	3 per Trafo

Dimensie: V2G, N-1

Categorie	Spanning & Grens	Parameters	Afmetingen (B x L x H)	Aantal
MS Transformator	Primair: 110 kV\\Secundair: 10.0 kV Grens: 4000 kVA	Schakeling: YNd11 Korstluitspanning: 11% Kortsluitverlies: 28000 W	B: 2000 mm L: 2500 mm H: 2600 mm	3
LS Transformator	Primair: 10 kV\\Secundair: 0.4 kV Grens: 630 kVA	Schakeling: Dyn11 Korstluitspanning: 4% Kortsluitverlies: 6500 W	B: 950 mm L: 1600 mm H: 1800 mm	12

Categorie	Spanning & Materiaal	Doorsnede & Aders	Parameters & Spanningsval	Kabels per Trafo
MS Cable	Spanning: 10.0 kV Materiaal: Aluminium	Doorsnede: 95 mm² Ader Aantal: 3	Max Amperage: 210 A Weerstand: 0.32 Ω/km Spanningsval: 133.3 V	2 per Trafo
LS Cable	Spanning: 0.4 kV Materiaal: Aluminium	Doorsnede: 240 mm² Ader Aantal: 4	Max Amperage: 300 A Weerstand: 0.125 Ω/km Spanningsval: 246.9 V	6 per Trafo